

OBRA: **VIVIENDA UNIFAMILIAR**

LOCALIDAD: **PIEDRAHITA, AVILA**

NIVEL **FORJADO 0 Y FORJADO 1**
:





COLOR: **GRIS**

GROSOR: **26 cm**

PANEL: **FJ.01**

CARA: **CARA SUPERIOR**

UNIDADES: **2**

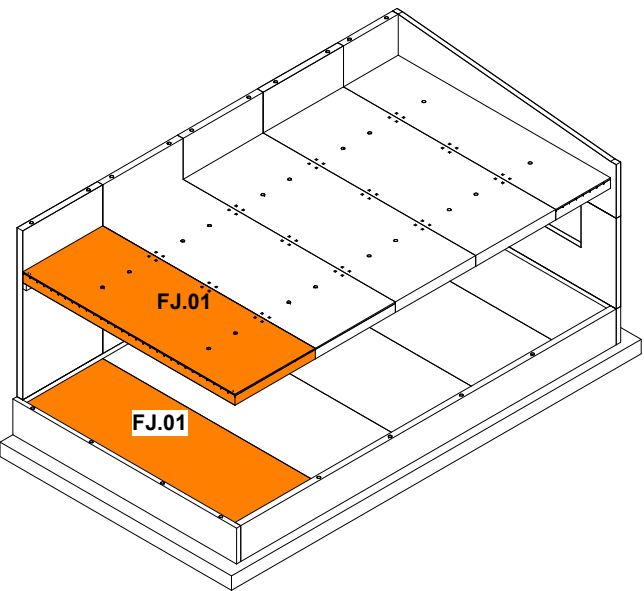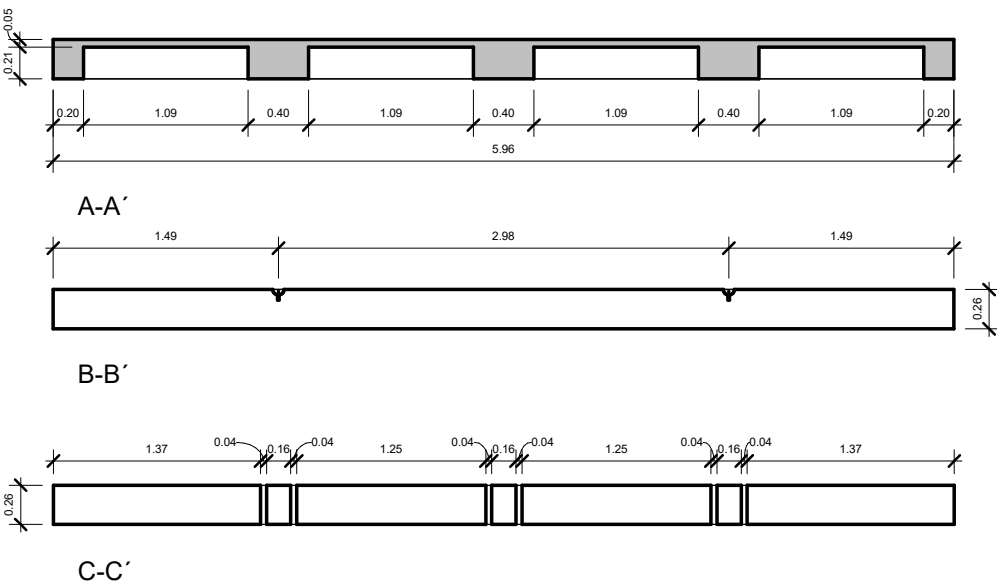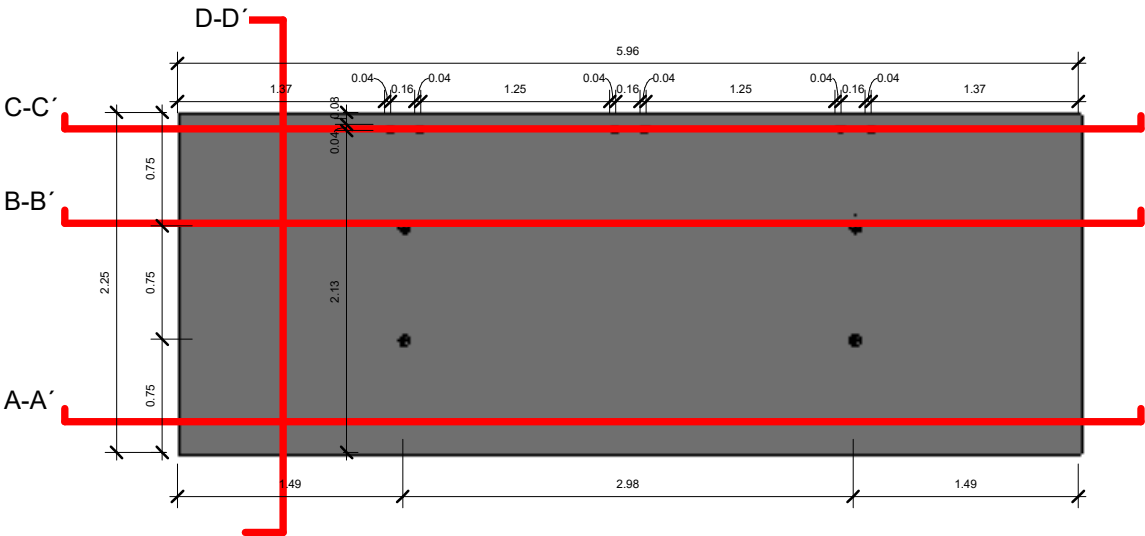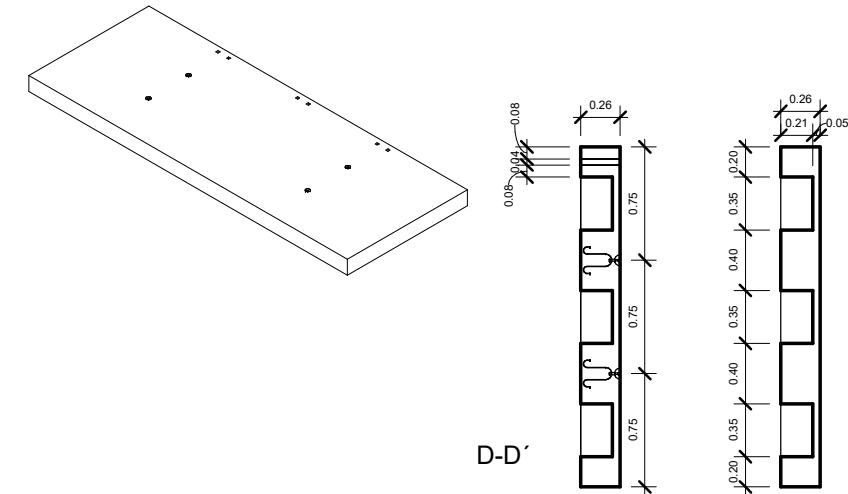

OBRA: **VIVIENDA UNIFAMILIAR**

LOCALIDAD: **PIEDRAHITA, AVILA**

NIVEL: **FORJADO 0 Y FORJADO 1**




COLOR: **GRIS**

GROSOR: **0.26 CM**

PANEL: **FJ.01**

CARA: **CARA MOLDE**

UNIDADES: **2**

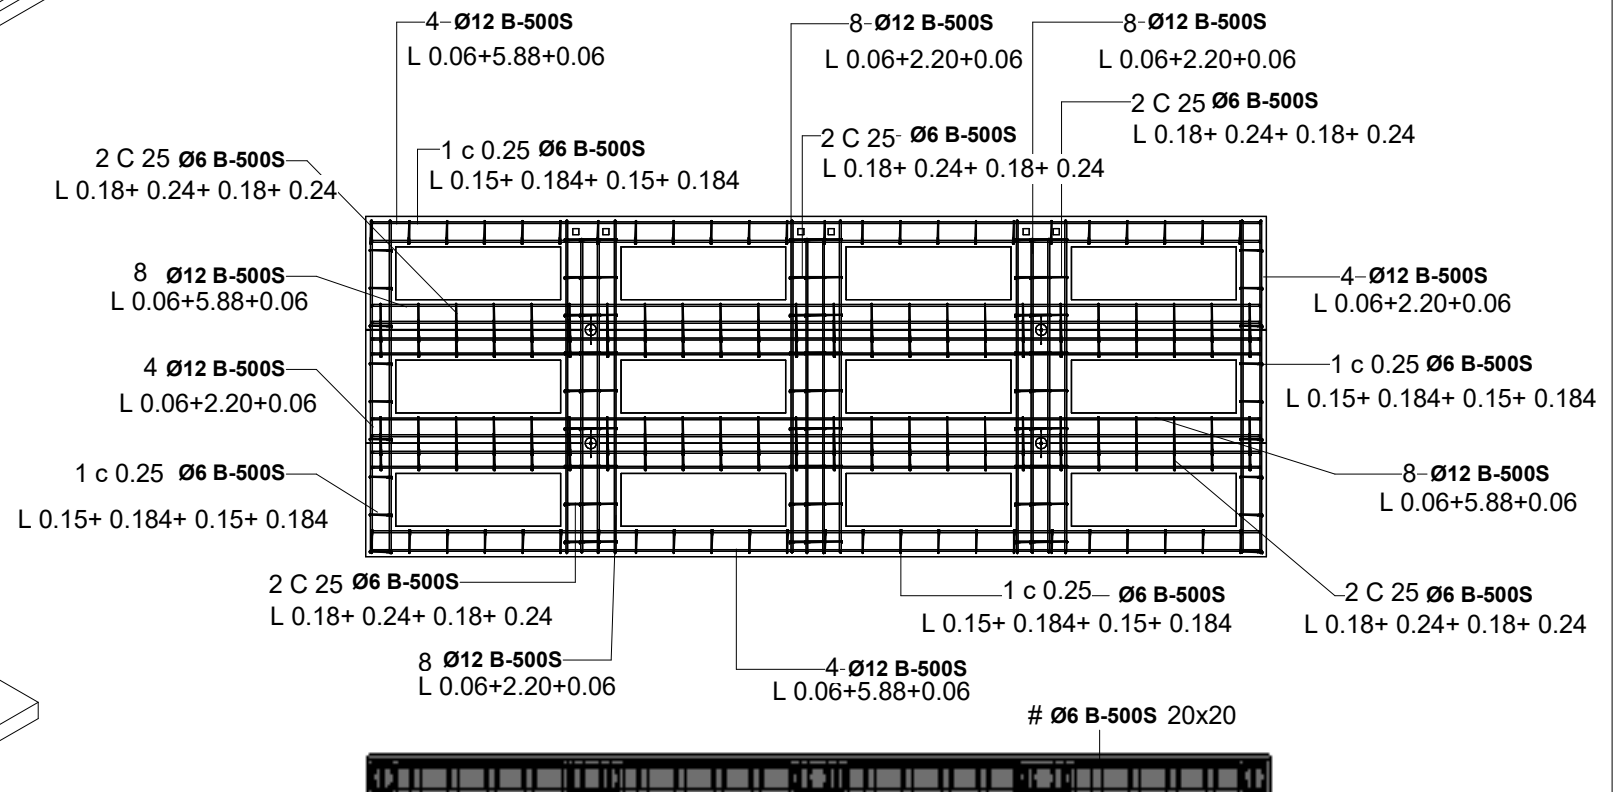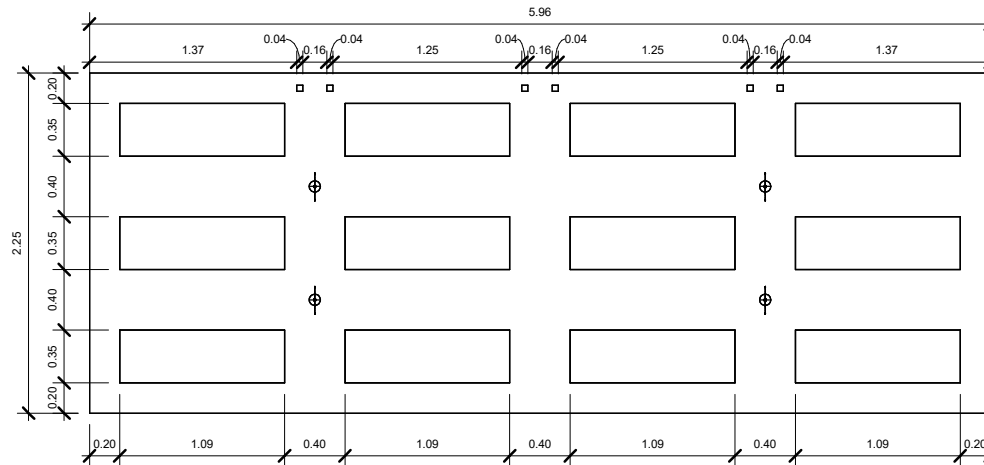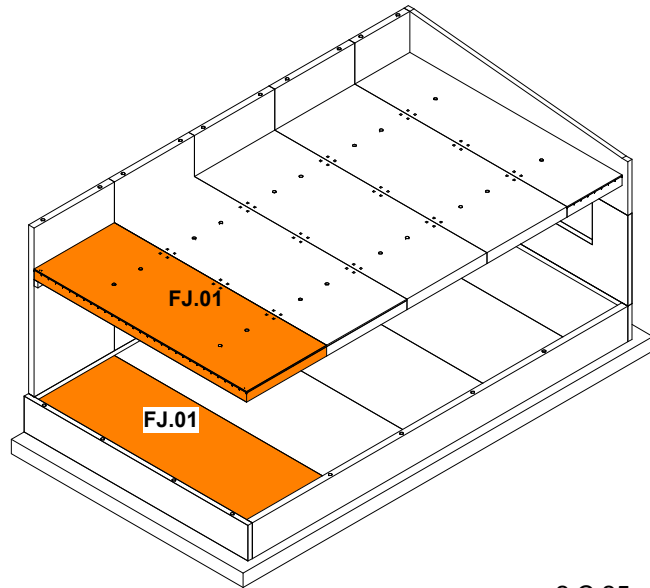

OBRA: **VIVIENDA UNIFAMILIAR**

LOCALIDAD: **PIEDRAHITA, AVILA**

NIVEL: **FORJADO 0 Y FORJADO 1**
:


COLOR: **GRIS**

GROSOR: **0.26 CM**

PANEL: **FJ.01**

CARA: **DETALLES**

UNIDADES: **2**

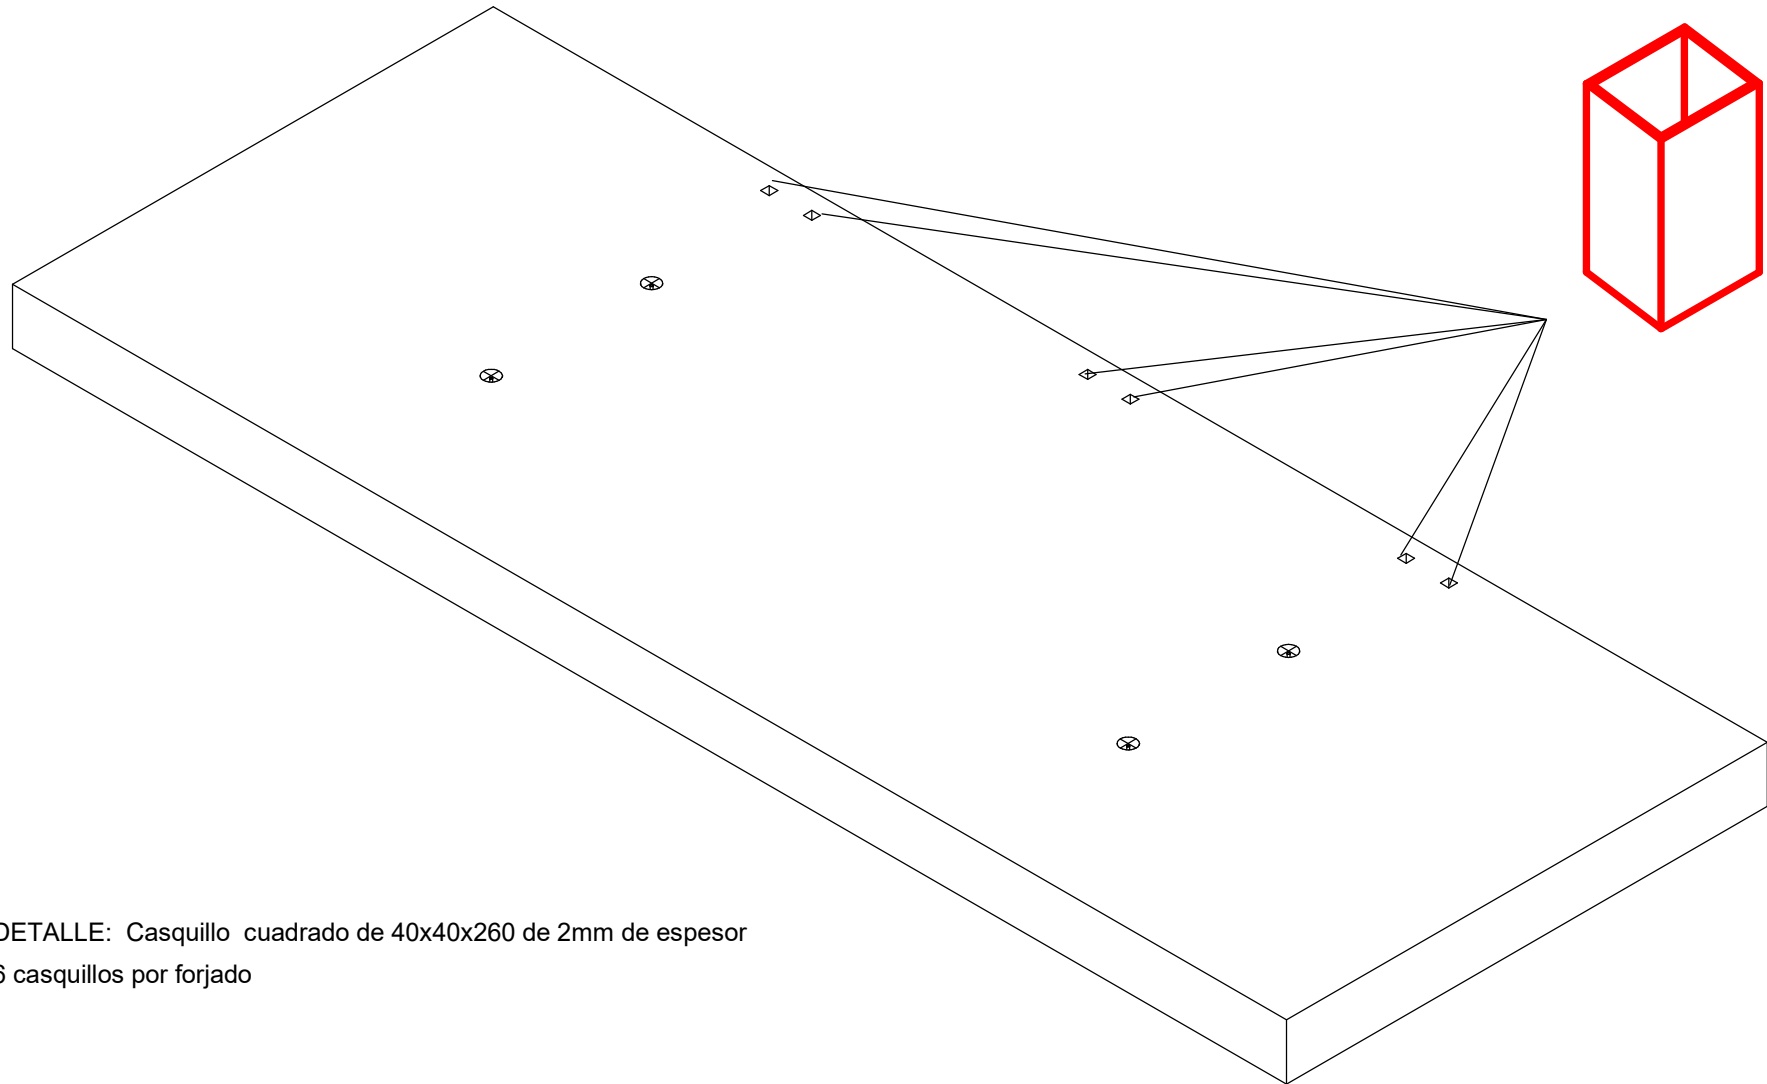

DETALLE: Casquillo cuadrado de 40x40x260 de 2mm de espesor
6 casquillos por forjado

OBRA: **VIVIENDA UNIFAMILIAR**

LOCALIDAD: **PIEDRAHITA, AVILA**

NIVEL **FORJADO 0 Y FORJADO 1**
:





COLOR: **GRIS**

GROSOR: **0.26 CM**


PANEL: **FJ.02**

CARA: **CARA SUPERIOR**


UNIDADES: **6**

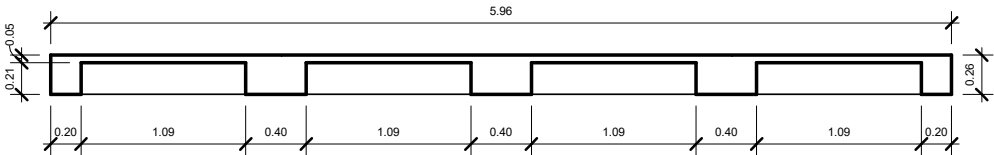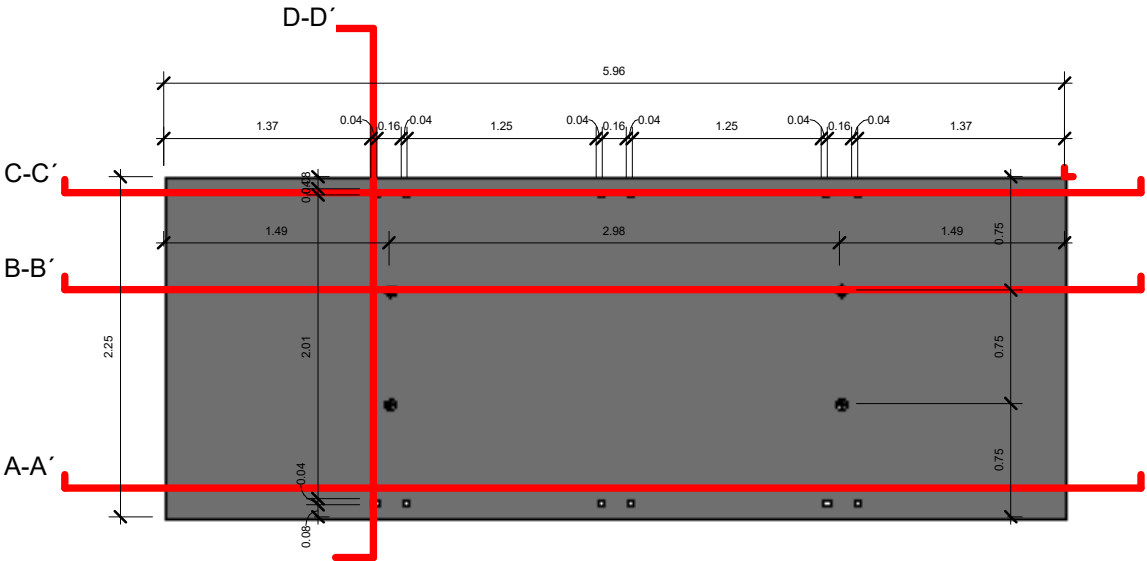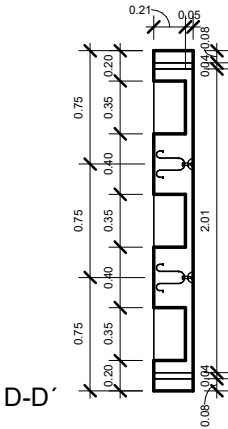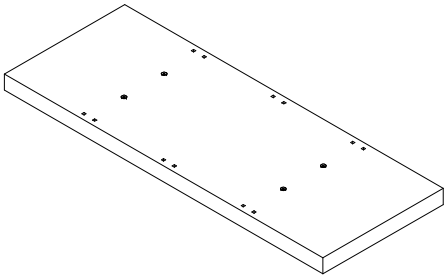


A-A'

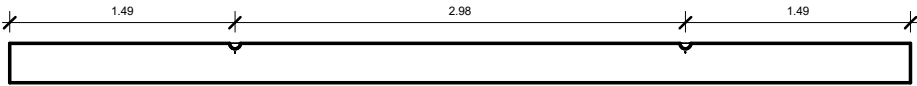

B-B'

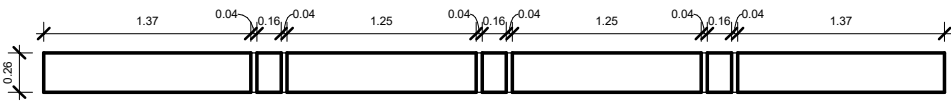

C-C'

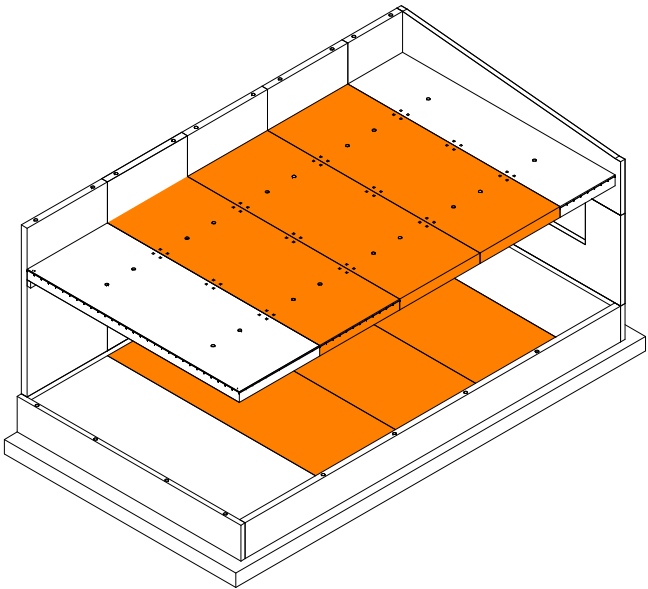

OBRA: **VIVIENDA UNIFAMILIAR**

LOCALIDAD: **PIEDRAHITA, AVILA**

NIVEL: **FORJADO 0 Y FORJADO 1**





COLOR: **GRIS**

GROSOR: **0.26 CM**

PANEL: **FJ.02**

CARA: **CARA MOLDE**

UNIDADES: **6**

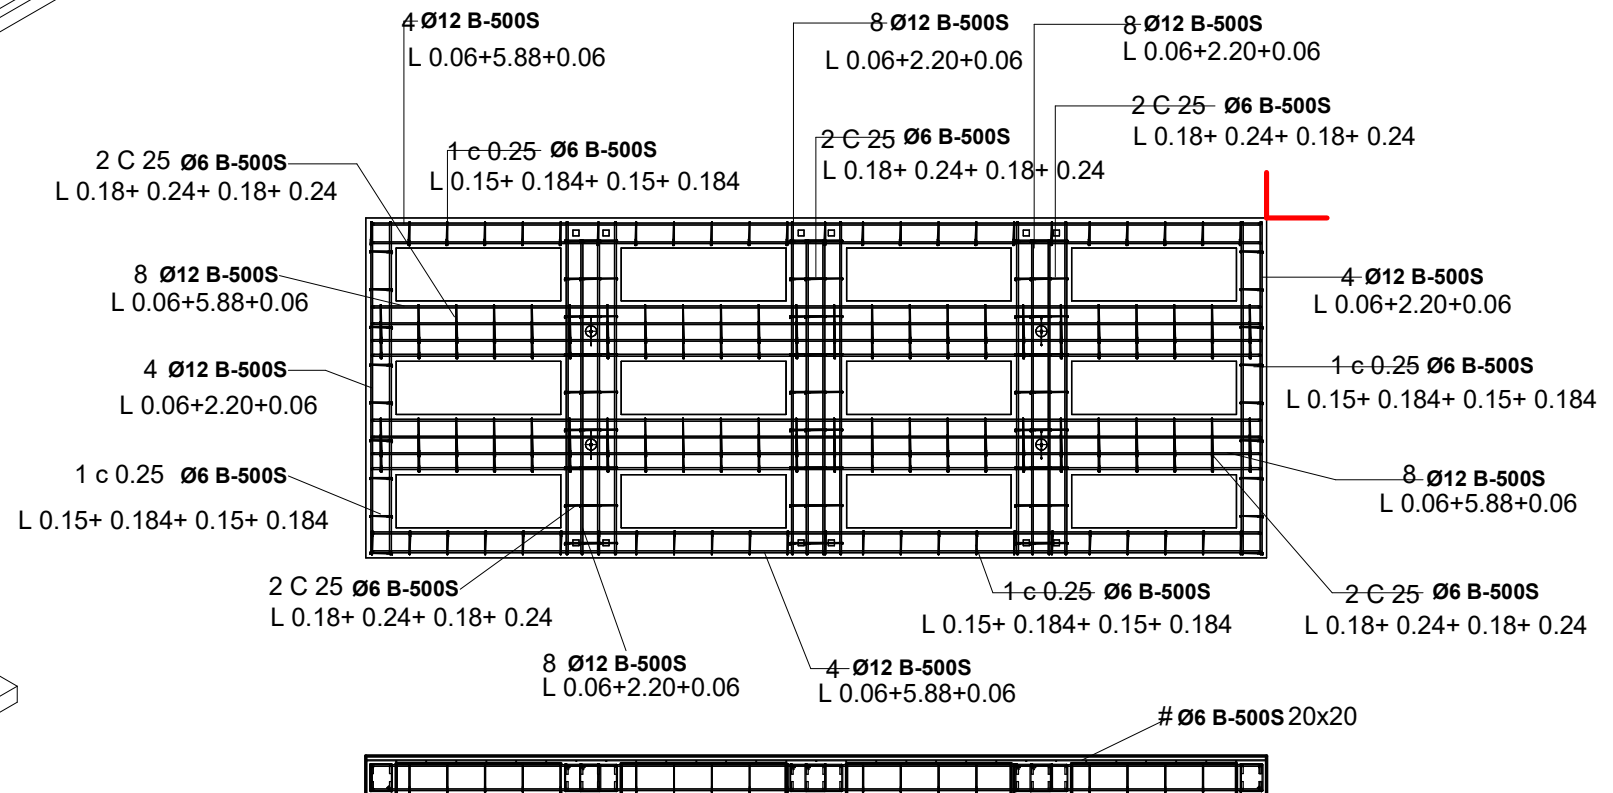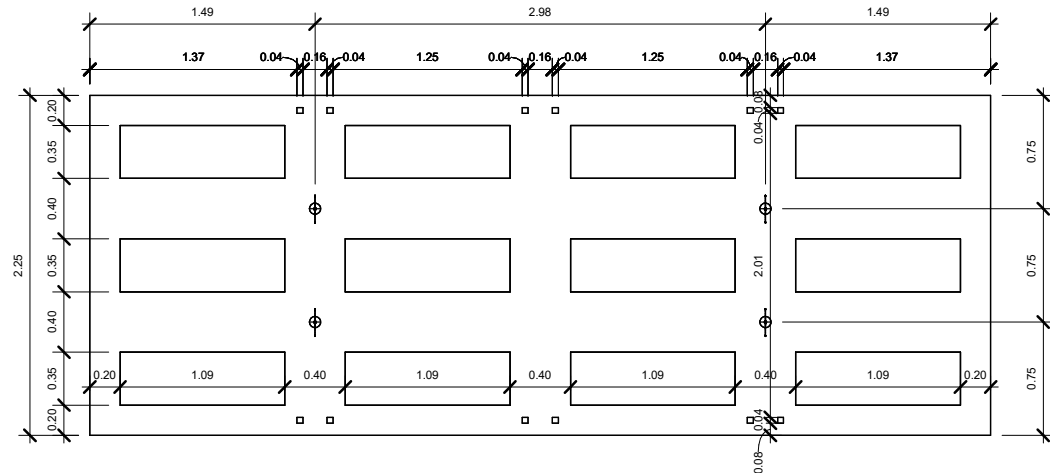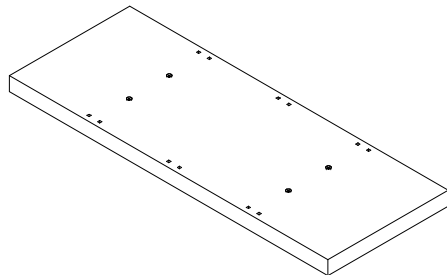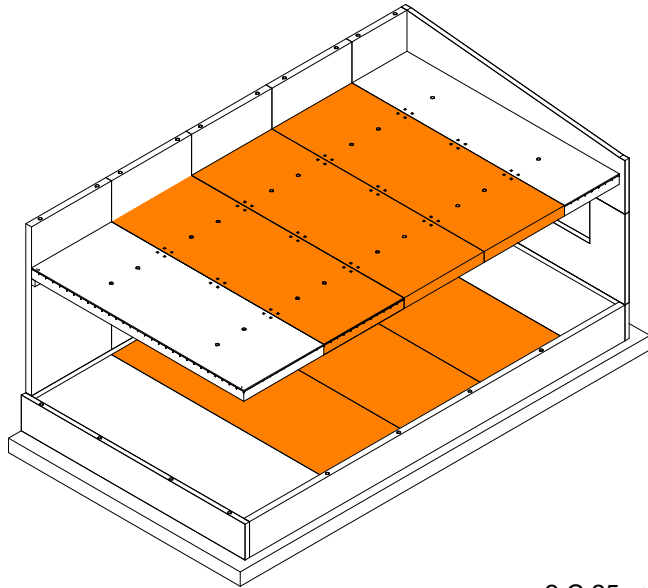

OBRA: **VIVIENDA UNIFAMILIAR**

LOCALIDAD: **PIEDRAHITA, AVILA**

NIVEL FORJADO 0 Y FORJADO 1
:


COLOR: GRIS

GROSOR: 0.26 CM

PANEL: **FJ.02**

CARA: **DETALLE**

UNIDADES: 6

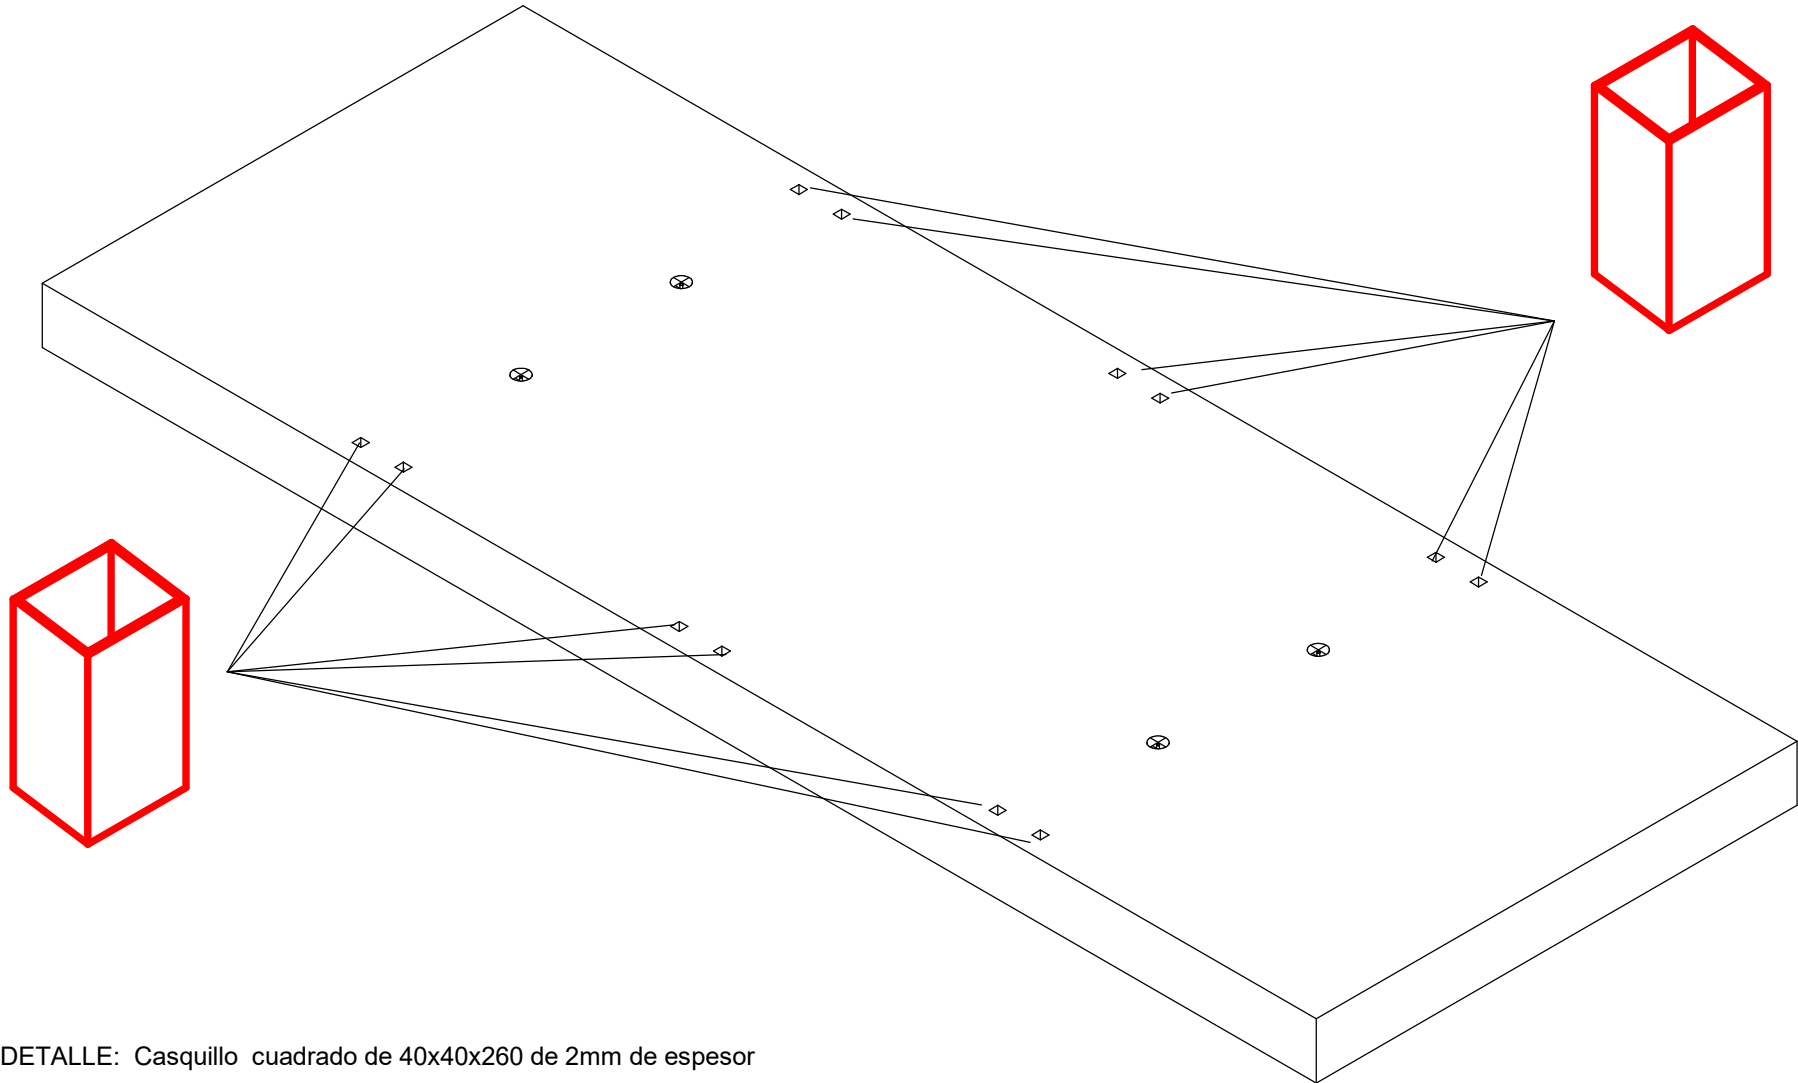

DETALLE: Casquillo cuadrado de 40x40x260 de 2mm de espesor
12 casquillos por forjado

OBRA: **VIVIENDA UNIFAMILIAR**

LOCALIDAD: **PIEDRAHITA, AVILA**

NIVEL **FORJADO 0 Y FORJADO 1**
:


COLOR: **GRIS**

GROSOR: **0.26 CM**

PANEL: **FJ.03**

CARA: **CARA SUPERIOR**

UNIDADES: **2**

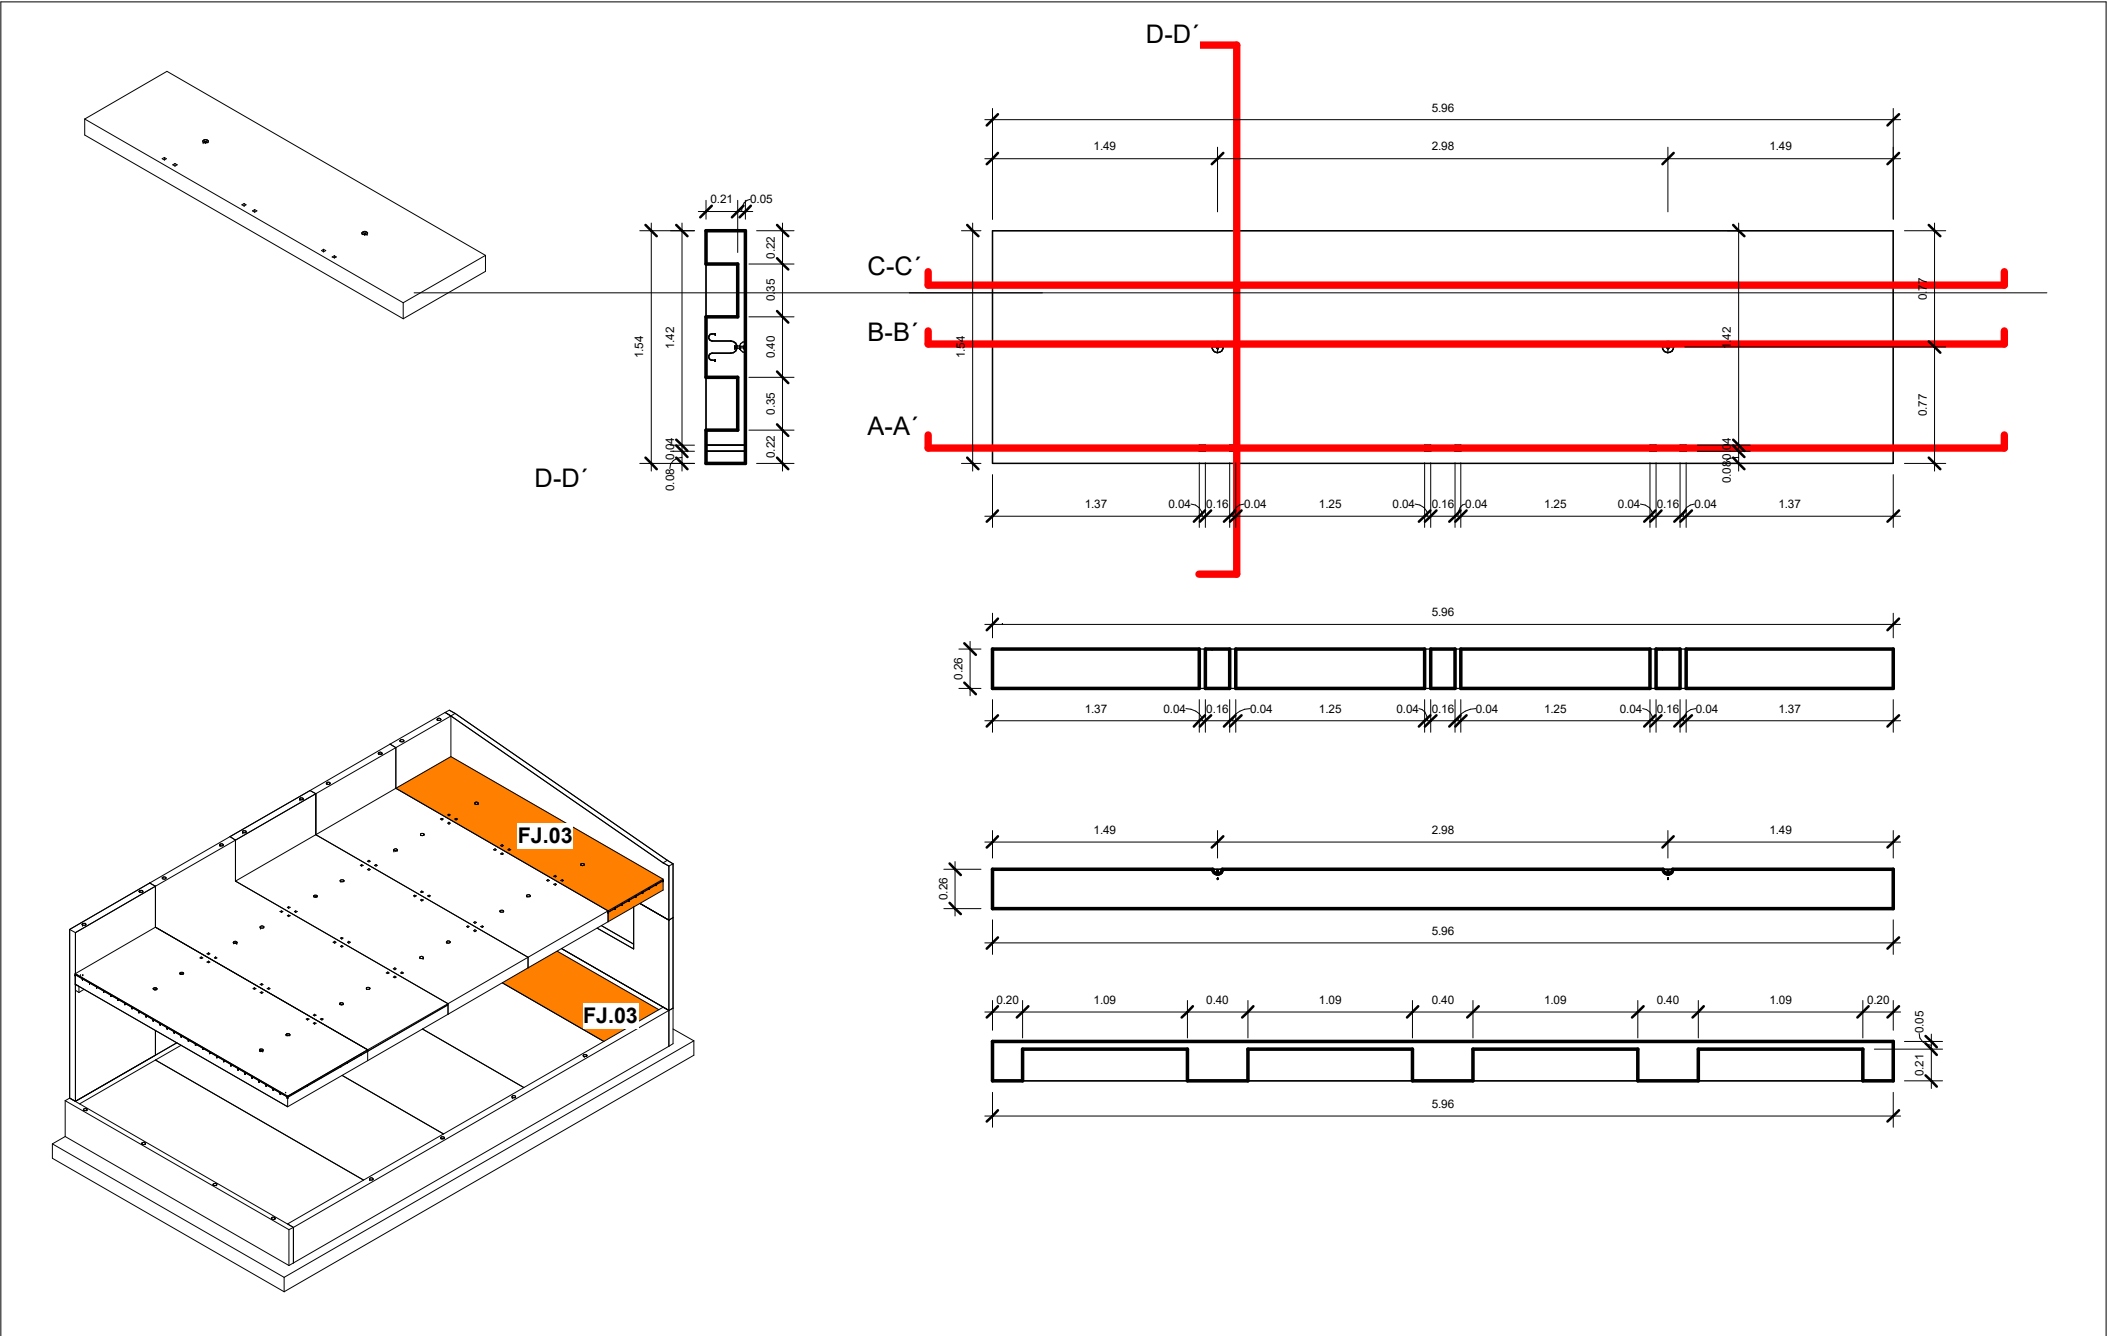

OBRA: **VIVIENDA UNIFAMILIAR**

LOCALIDAD: **PIEDRAHITA, AVILA**

NIVEL FORJADO 0 Y FORJADO 1



COLOR: GRIS

GROSOR: 0.26 CM

PANEL: **FJ.03**

CARA: **CARA MOLDE**

UNIDADES: 2

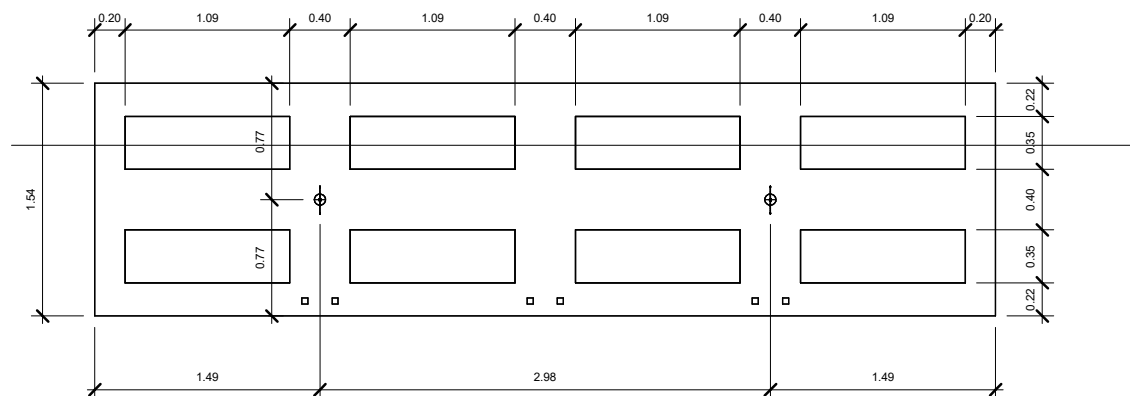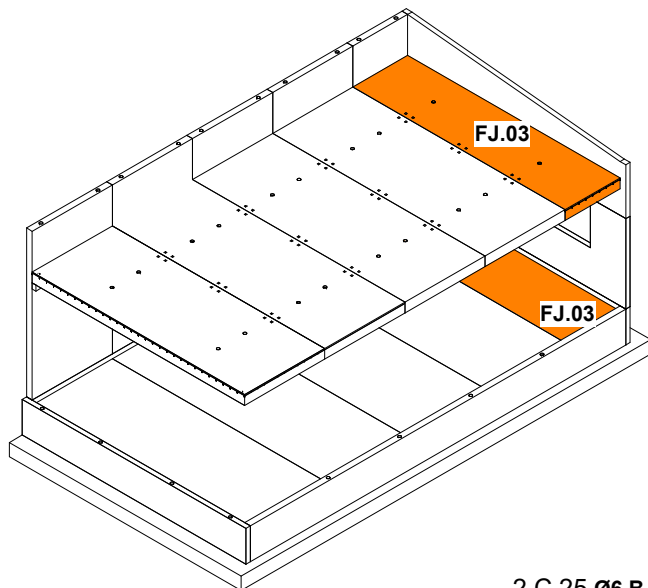

4 Ø6 B-500S
L 0.06+5.88+0.06

8 Ø12 B-500S
L 0.06+2.20+0.06

8-Ø12 B-500S
L 0.06+2.20+0.06

2 C 25 Ø6 B-500S
L 0.18+ 0.24+ 0.18+ 0.24

1c 0.25 Ø6 B-500S
L 0.15+ 0.184+ 0.15+ 0.184

2 C 25 Ø6 B-500S
L 0.18+ 0.24+ 0.18+ 0.24

2-C 25 Ø6 B-500S
L 0.18+ 0.24+ 0.18+ 0.24

8 Ø12 B-500S
L 0.06+5.88+0.06

4 Ø12 B-500S—
L 0.06+2.20+0.06

1 c 0.25Ø6 B-500S
L 0.15+ 0.184+ 0.15+ 0.184

B-500S

~~2 C 25~~ Ø6 B-500S

~~2 C 25 Ø6 B-500S~~

~~4 Ø12 B-500S~~
L 0.06+2.20+0.06

1 c 0.25 Ø6 B-500S
L 0.15+ 0.184+ 0.15+ 0.184

8-Ø12 B-500S
L 0.06+5.88+0.06

2 C 25 Ø6 B-500S
L 0.18+ 0.24+ 0.18+ 0.24



1 c 0.25 Ø6 B-500S
L 0.15+ 0.184+ 0.15+ 0.184

2 C 25 Ø6 B-500S
L 0.18+ 0.24+ 0.18+ 0.24

8-Ø12 B-500S
L 0.06+2.20+0.06

4 Ø12 B-500S
L 0.06+5.88+0.06

Ø6 B-500S 20x20

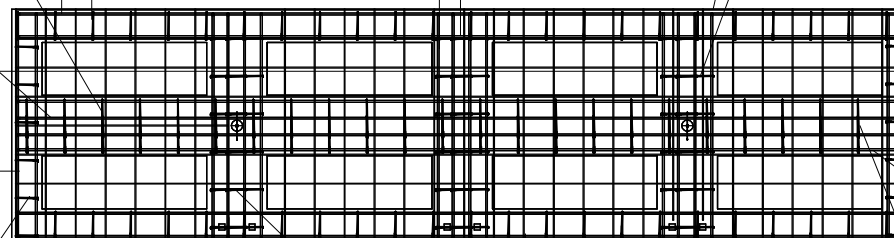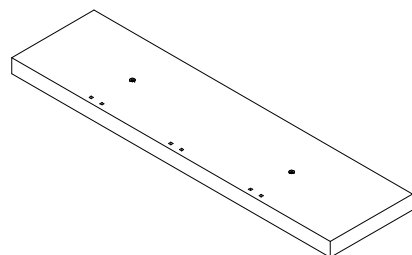

OBRA: **VIVIENDA UNIFAMILIAR**

LOCALIDAD: **PIEDRAHITA, AVILA**

NIVEL FORJADO 0 Y FORJADO 1
:



COLOR: GRIS

GROSOR: 0.26 CM

PANEL: **FJ.03**

CARA: **DETALLE**

UNIDADES: 2

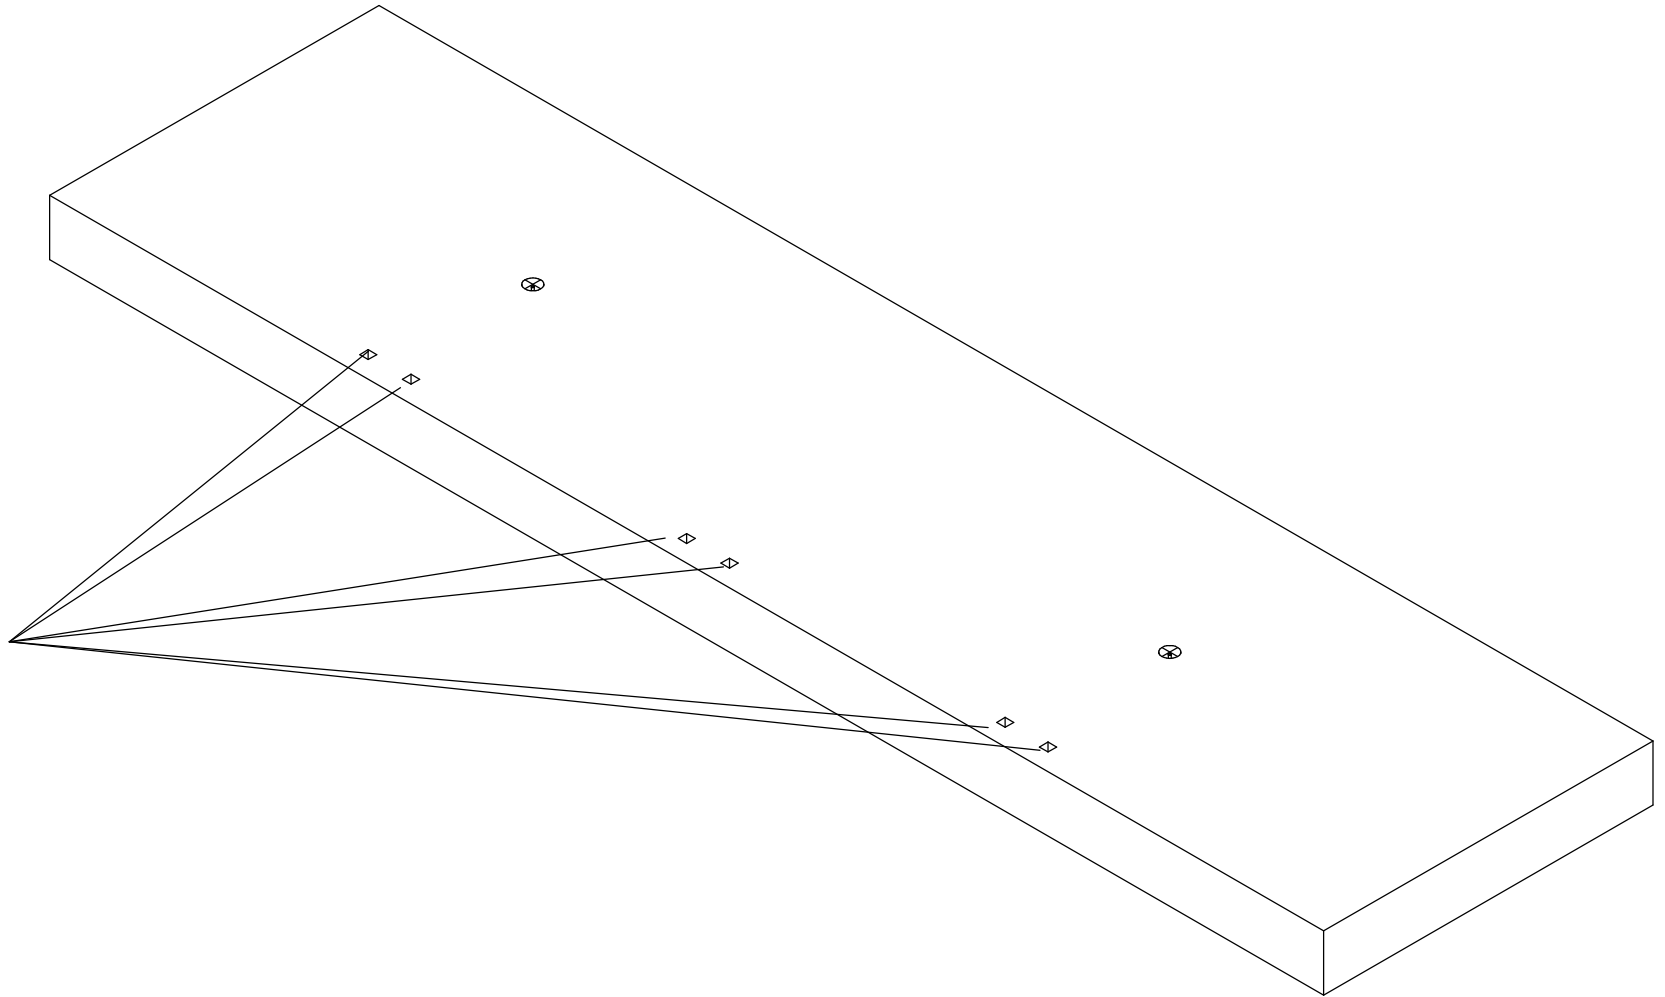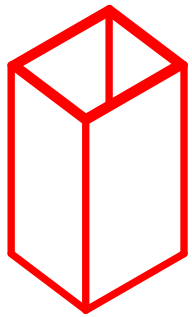

DETALLE: Casquillo cuadrado de 40x40x260 de 2mm de espesor
6 casquillos por forjado